
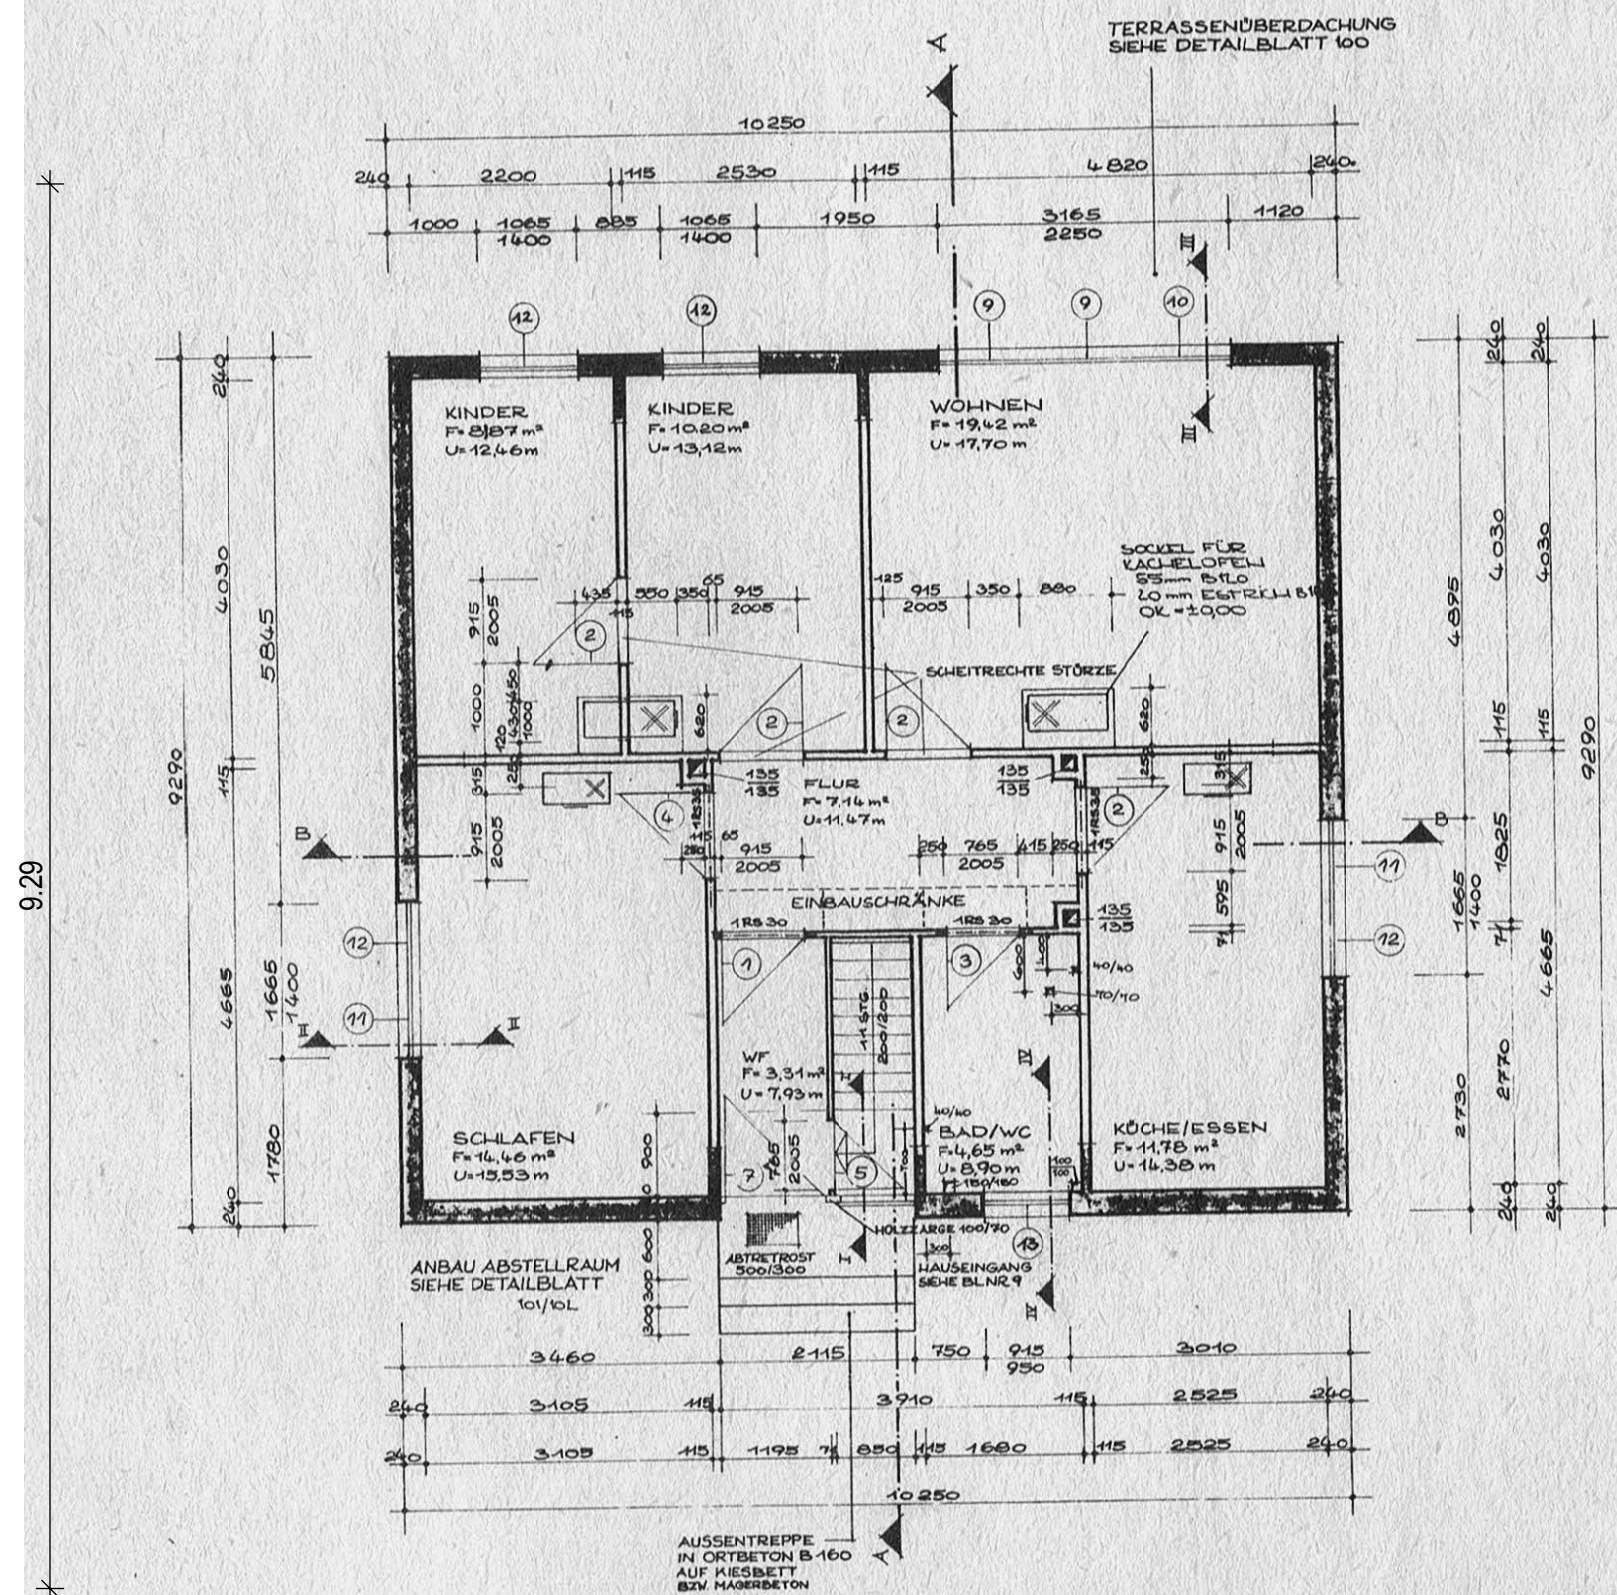
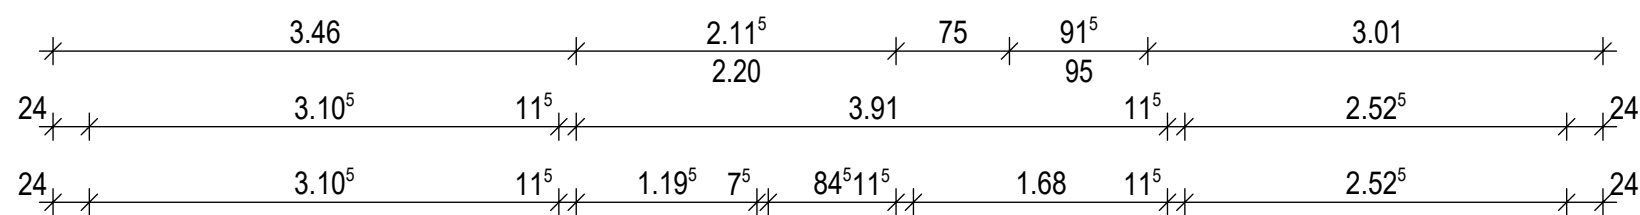


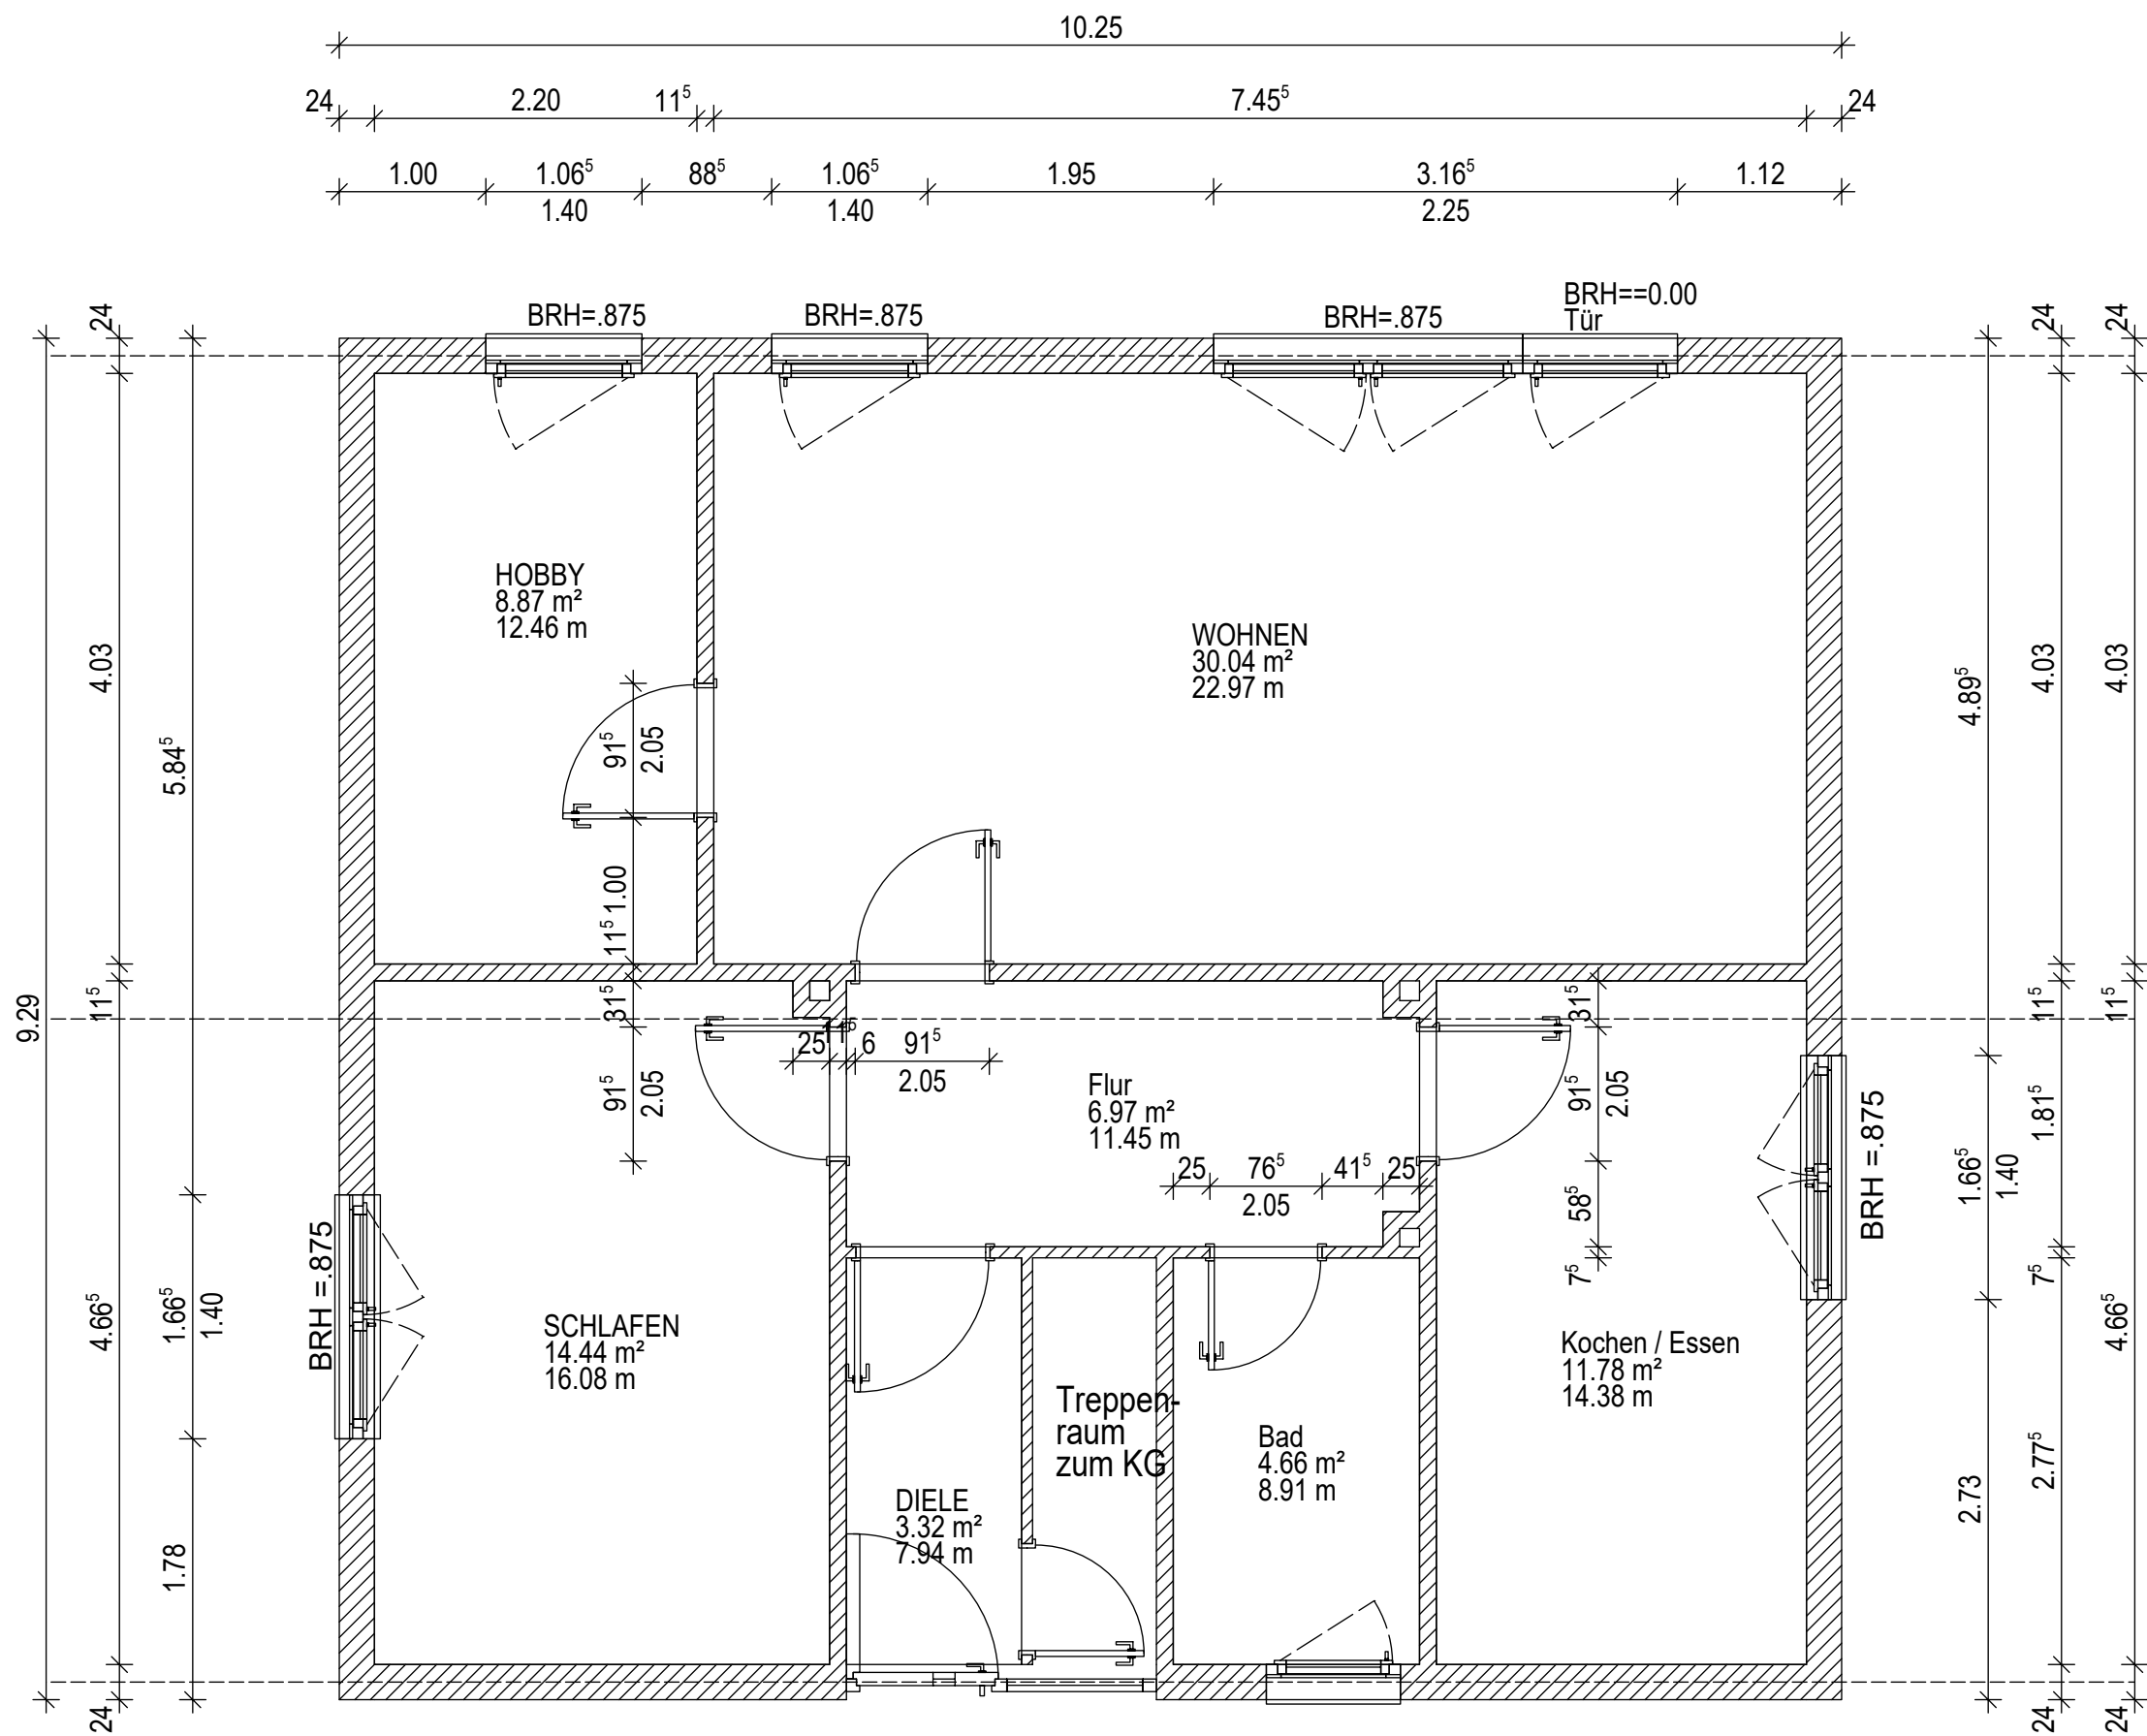

A	07.05.2025	Ulrich	Neumann	Eingabe der Pläne in CAD durch Architekt nach Handzeichnungen von VEB Landbauprojekt	
Index	Datum	Bearbeiter	Prüfer	Index-Notiz	
Projekt: Sanierung und Umbau eines Einfamilienhauses Klaus - Groth - Straße 12 17489 Hansestadt Greifswald					Projektnummer: 01HGW2025
Planinhalt: Grundriss ERDGESCHOSS					Plannummer: 403
Planungsstand: Aufmaßplan Darstellungsart: Grundriss					Maßstab: 1 : 50
Bauherr: Familie Neumann Klaus - Groth - Straße 12 17489 Hansestadt Greifswald			Architekt: Architekturbüro Dirk Ulrich Eichenweg 3A 18586 Ostseebad Göhren		Plandatum: 07.05.2025
freigegeben: Neumann			Datum:		Index: A